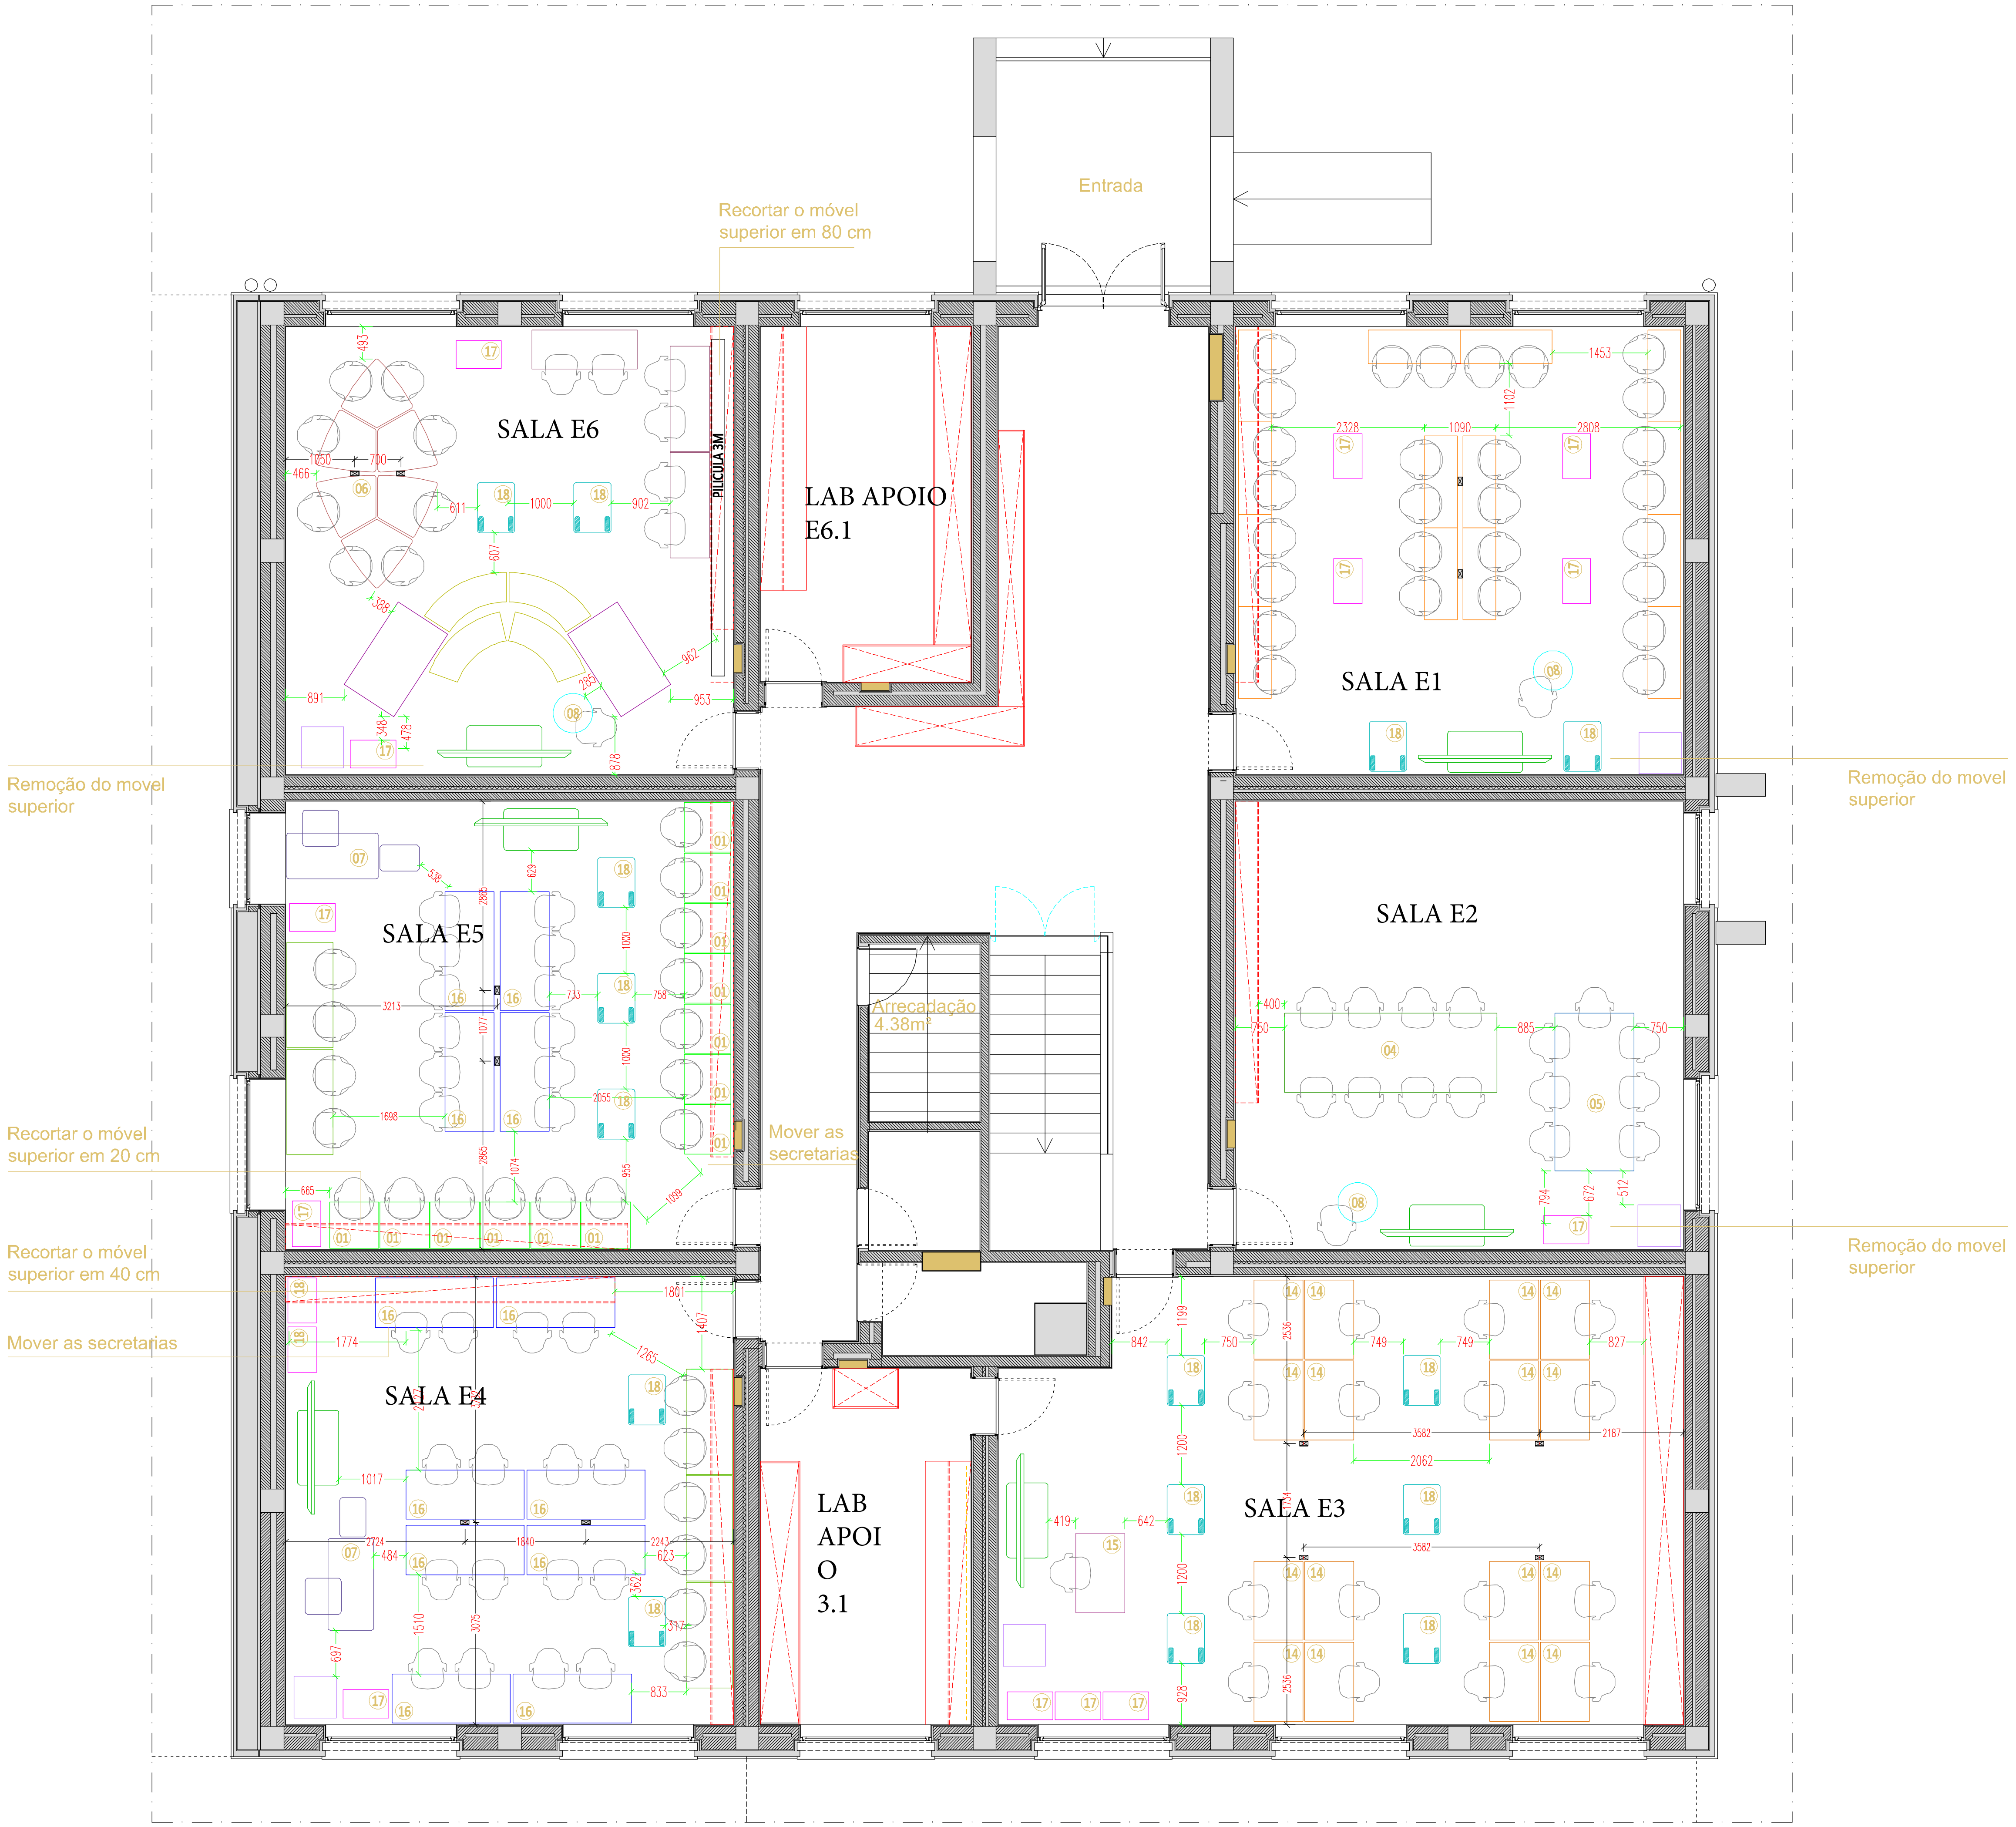
Entrada
Recortar o móvel superior em 80 cm
SALA E6
LAB APOIO E6.1
PELÍCULA 3M
SALA E1
Remoção do movel superior
SALA E5
SALA E2
Arrecadação 4.38m²
Mover as secretarias
Recortar o móvel superior em 20 cm
Remoção do movel superior
Recortar o móvel superior em 40 cm
Mover as secretarias
SALA E4
LAB APOIO 3.1
SALA E3
Remoção do movel superior

▬	CALLERO DUPLO GRATNELLS SSET13
▬	E32CPLUS - EU Aver E32C + 32 dispositivos
▬	RSET 01 Rover - 3 x F25
▬	PROMETHEAN 86"
▬	B1800900 Bancada 1800x750x900 mm (LxPxA) 2 x bloco elétrico com 3 tomadas monofásicas e 1 RJ45 Armário com 4 portas 450 mm c/ fechadura
▬	VTR 750 D Verd 750x700x750 mm (LxPxA)
▬	VTR F16 70 Verd 1600x700x740 mm (LxPxA)
▬	VTS 140 70R Verd 1400x700x750 mm (LxPxA) com púplito à direita
▬	BT11200900 - SCPU Bancada técnica 1200x750x900 mm (LxPxA) - s/ suporte CPU Altura fixa Bloco elétrico com 4 tomadas monofásicas e 2 x RJ45 Disjuntor de proteção Suporte para monitor
▬	BT11200900 - SBGCPU Bancada técnica 1200x750x900 mm (LxPxA) - s/ bloco de gavetas s/ suporte CPU Altura fixa Prateleira superior com iluminação Calha técnica com 4 tomadas monofásicas e 2 x RJ45 Disjuntor de proteção de calha elétrica Suporte para monitor
▬	N3L TDD 41D Mesa para professor - Altura 1050 mm, diametro 600 mm
▬	VTR 140 50 Verd 1400x500x750 mm (LxPxA)
▬	N4M 109 5N0 FrameFour Bench 3222x1200x1050 mm (LxPxA)
▬	N4M 109 5H0 FrameFour Bench 2400x1200x1050 mm (LxPxA)
▬	GAC100 Bancada ACTIFLEX 1500x900x780 mm (LxPxA)
▬	N3L T50 030 B - Free 1600x600x780 mm (LxPxA)
▬	AAC115 Actiflex Wave - Armário Curvo
▬	MESA DIAMOND

▬ Existente ▬ Construir ▬ Quadro Eletrico

DESIGUAL
arquitectura de interiores
Rua D. Afonso Henriques, nº 4448 | 4445-641 Ermesinde - Portugal
tlm.: +351. 22 975 55 57 > email: geral@desigual.pt

Autor do Projecto:

Requerente : ESCOLA SECUNDÁRIA DE RIO TINTO

Obra : Intervenção interior 015-2023 epr

Localização : Rio Tinto Rio Tinto

Especialidade			Titulo do desenho		Data
Arquitectura			PLANTA MOBILÍARIOS		15- 09 - 2025
			Nº Des.		Escala
	Arq	Ep	02		1:100